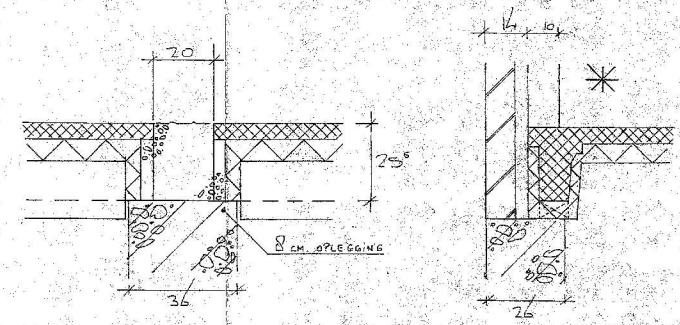
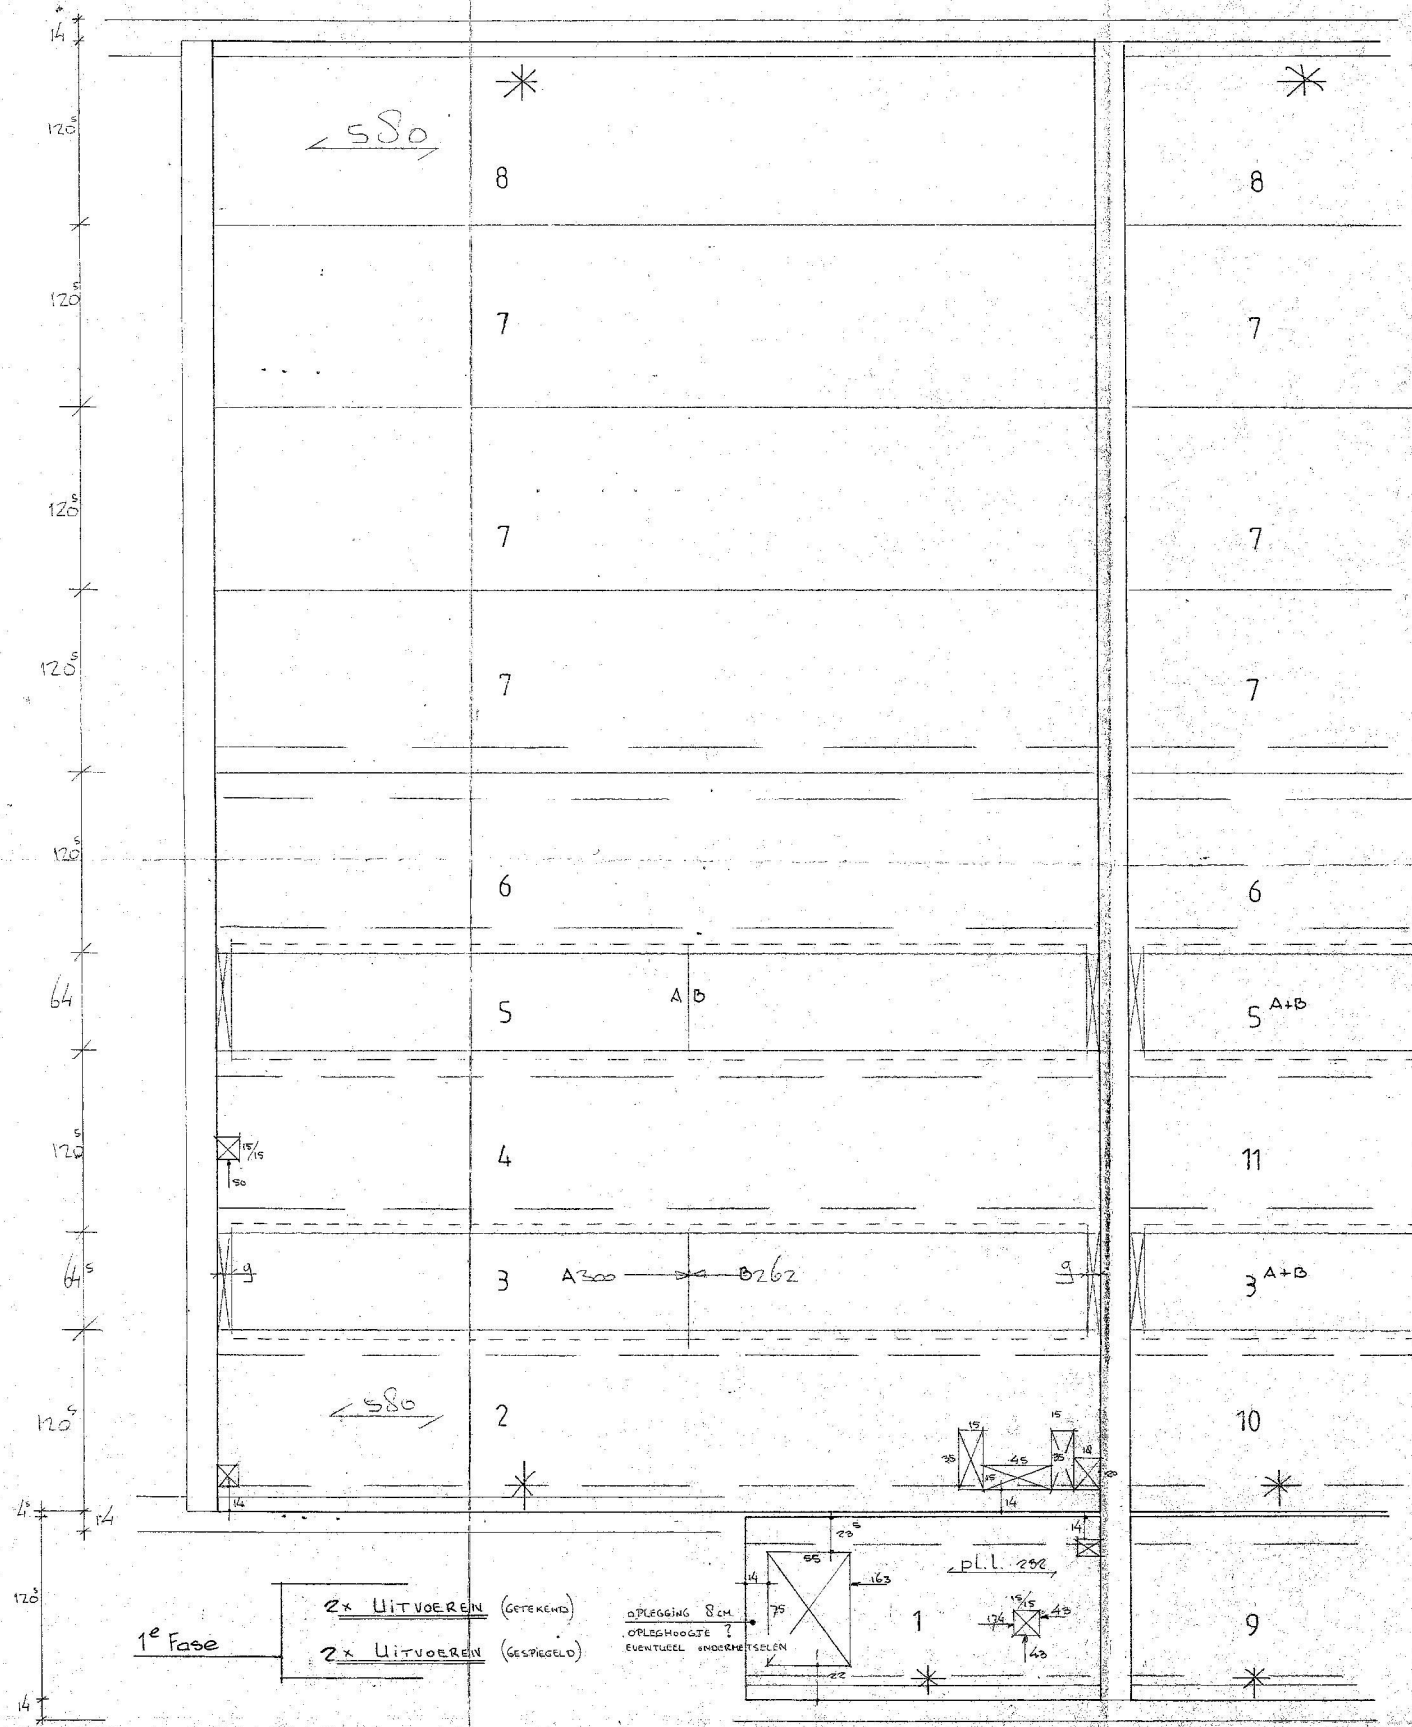


WELKE UITBREIDINGEN KOMEN VOOR? EN HOEVAK IN GET. EN GESP. SITUATIE?

→ EXTRA PLATEN?

→ LANGERE PLATEN?

VOOR- EN ACHTERGEVEUGELK ZIJN ALTIJD 6 CM LAGER

OPLEGGHOOGTE IS 25⁵ CM.

Gezien: 6 FEB 1985
1x PASPL. NETTO BREEDTE BOWW. en Woningbouw VOORHOUT

* SPONNING DICHT
BETONNOKKEN IN ISOLATIE ONDER RIS MAX 150M HOOG NIET TEG. OPLEG

R = 2.0 betonkwaliteit B 37.5	B = FeB 500
B.S.F. BV	tel. 076 - 874652 postbus 28627 4800 CB BREDAA
werk: 401 Woningen van Dordrecht B.S. te Voorhout	Noordland
betreft: MANTA systeemvloer voor de begane grond Woningtype M1	NR 1341 RZ-E BL- A
get. t.c. dd 15-11-85 gewijz. d. d. 12-12-85	tel. 11 schad. 1.20.10