


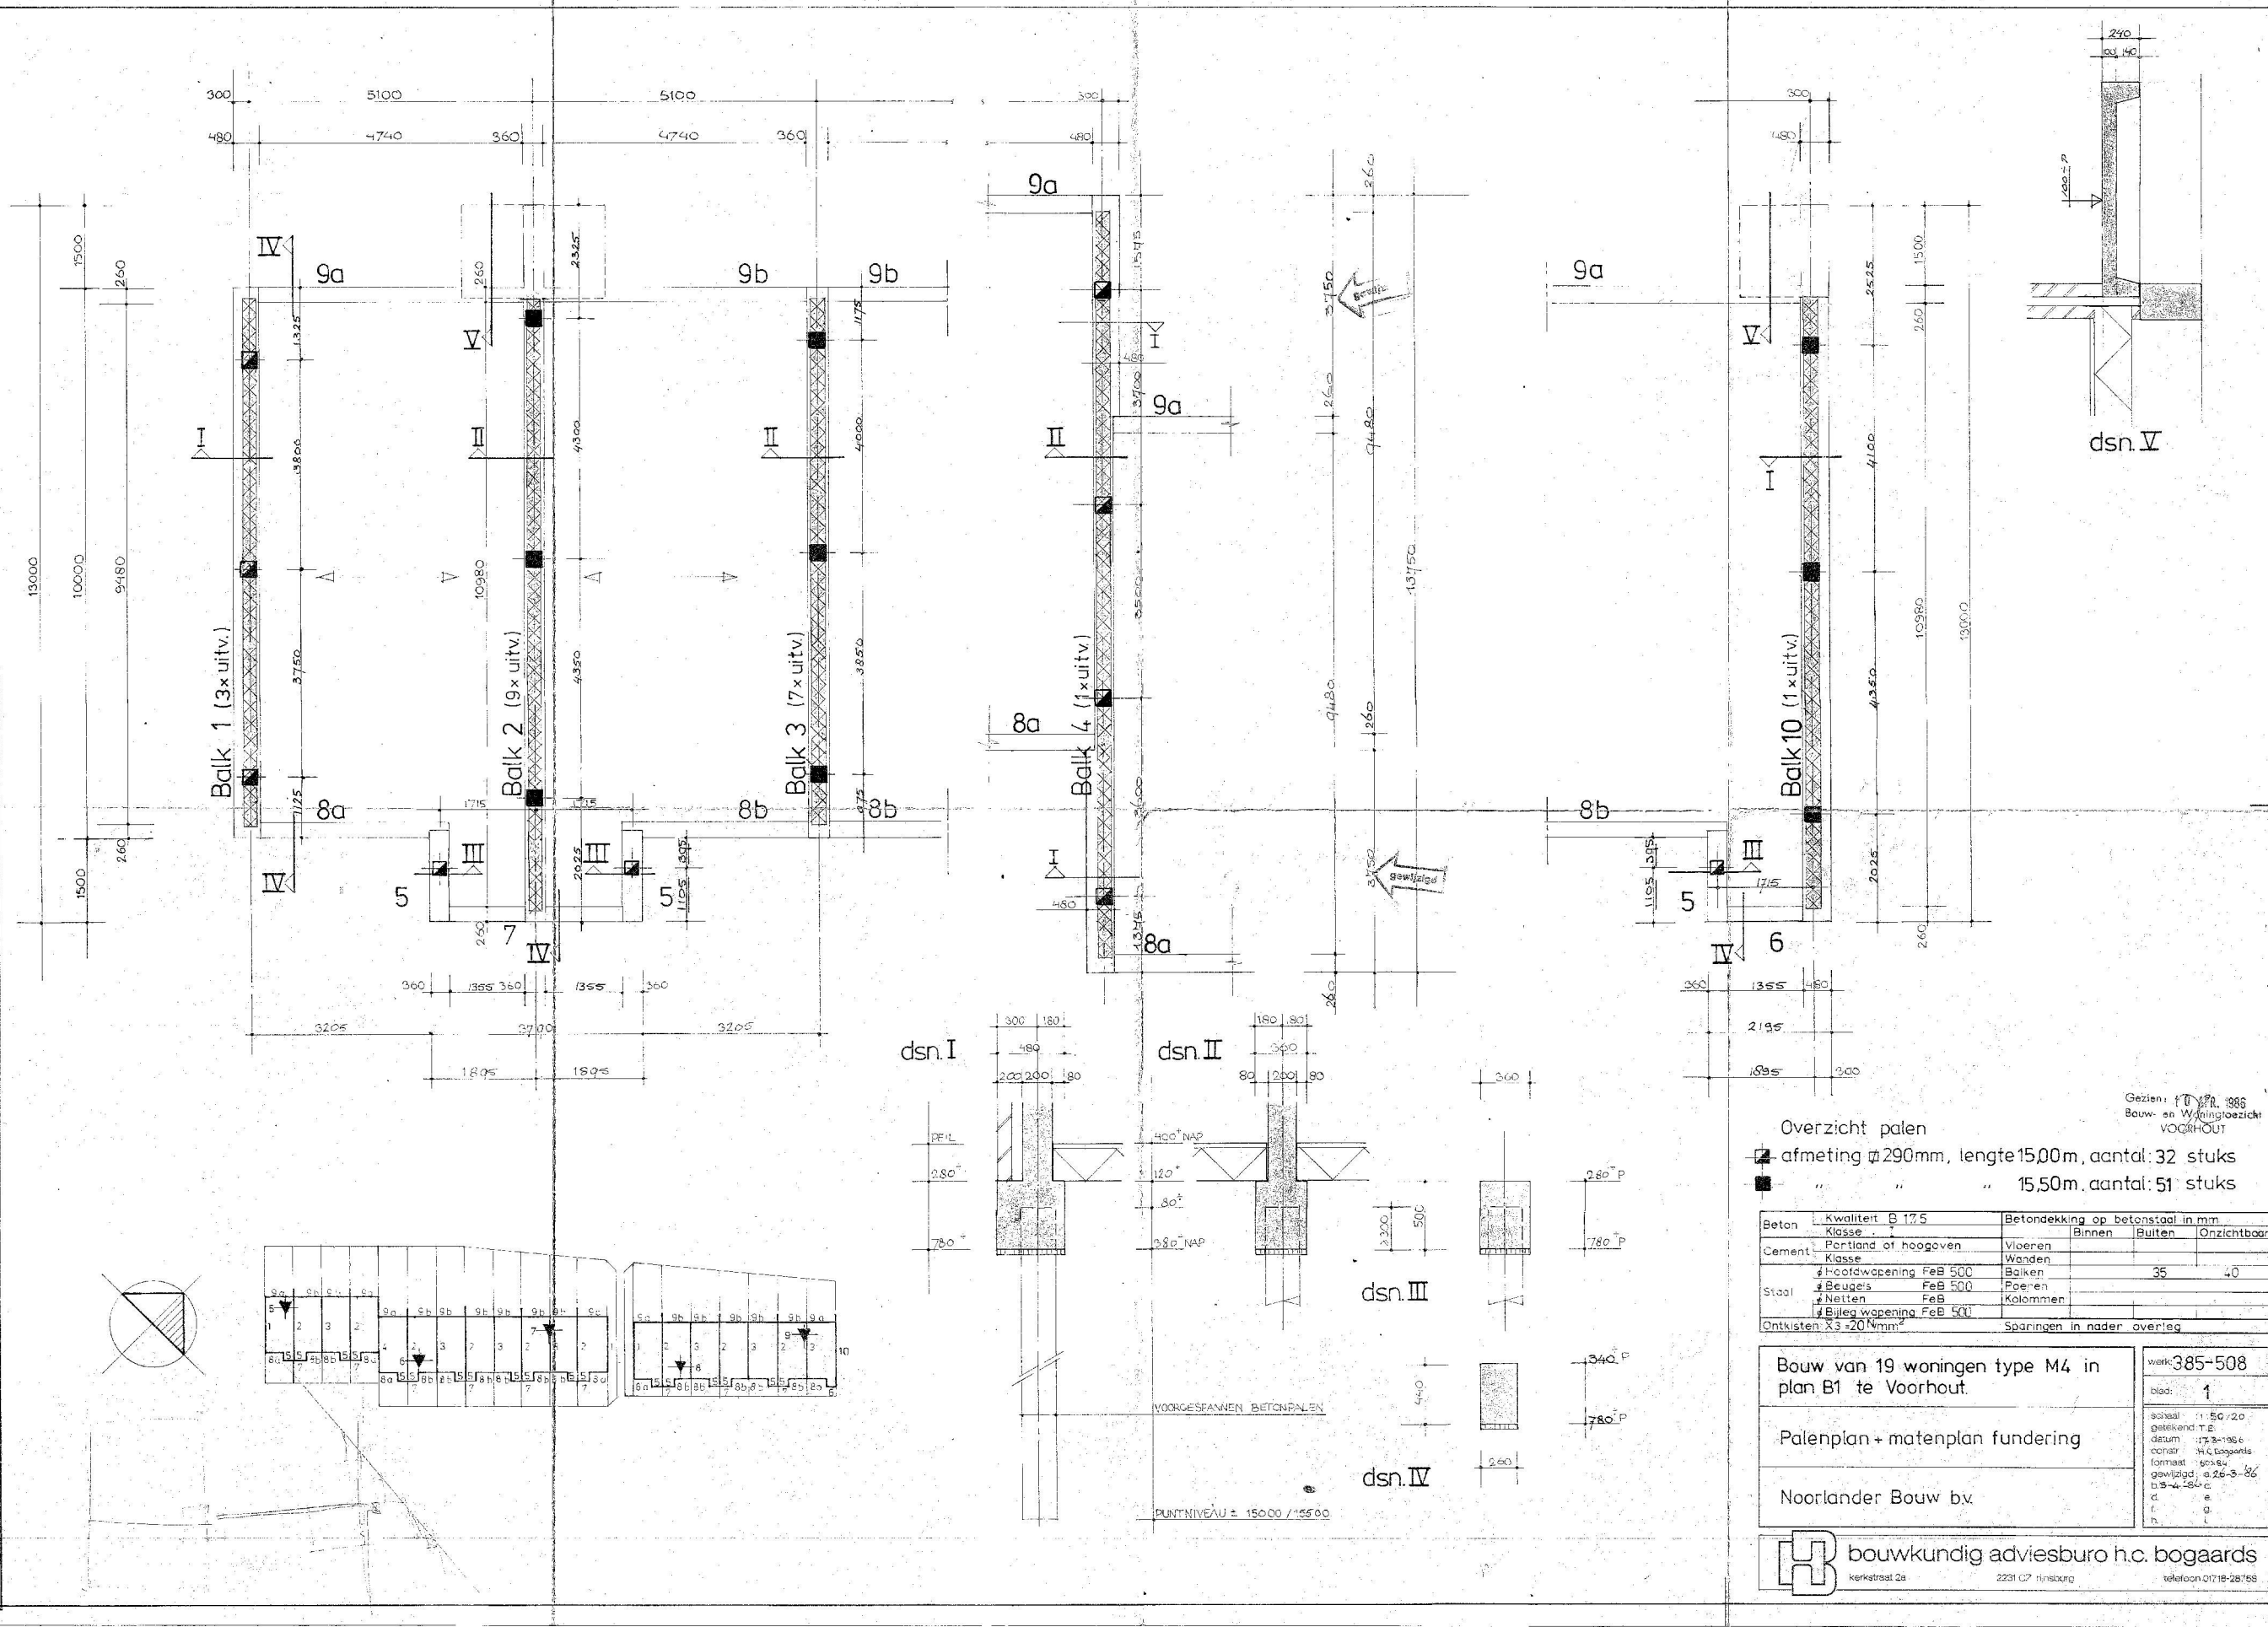

Gezien: 17.12.1986
Bouw- en Woningtoezicht
VOORHOUT

Overzicht palen
 ■ afmeting $\varnothing 290\text{mm}$, lengte 15,00m, aantal: 32 stuks
 ■ " " " " 15,50m, aantal: 51 stuks

Beton	Kwaliteit B 17,5	Betondekking op betonstaal in mm			
Klasse	Portland of hoogoven	Vloeren	Binnen	Buiten	Onzichtbaar
Cement	Klasse	Wanden			
Staal	Hoofdwapening FeB 500	Balken	35	40	
	Beugels FeB 500	Poeren			
	Netten FeB	Kolommen			
	Bijleg wapening FeB 500				

Ontkisten $X3 \times 20\text{Nmm}^2$ Sparringen in nader overleg

Bouw van 19 woningen type M4 in plan B1 te Voorhout.

Palenplan + matenplan fundering

Noorlander Bouw bv.

werk: 385-508
 blad: 1
 schaal: 1:50 / 2:0
 getekend: T.E.
 datum: 17-3-1986
 ontworpen: H.C. Bogaards
 formaat: A0
 gewijzigd: a.26-3-86
 b.3-4-86
 c.
 d.
 e.
 f.
 g.
 h.

bouwkundig adviesburo h.c. bogaards
 kerkestraat 2a 2231 CZ HINSBEEK telefoon 01718-28758