



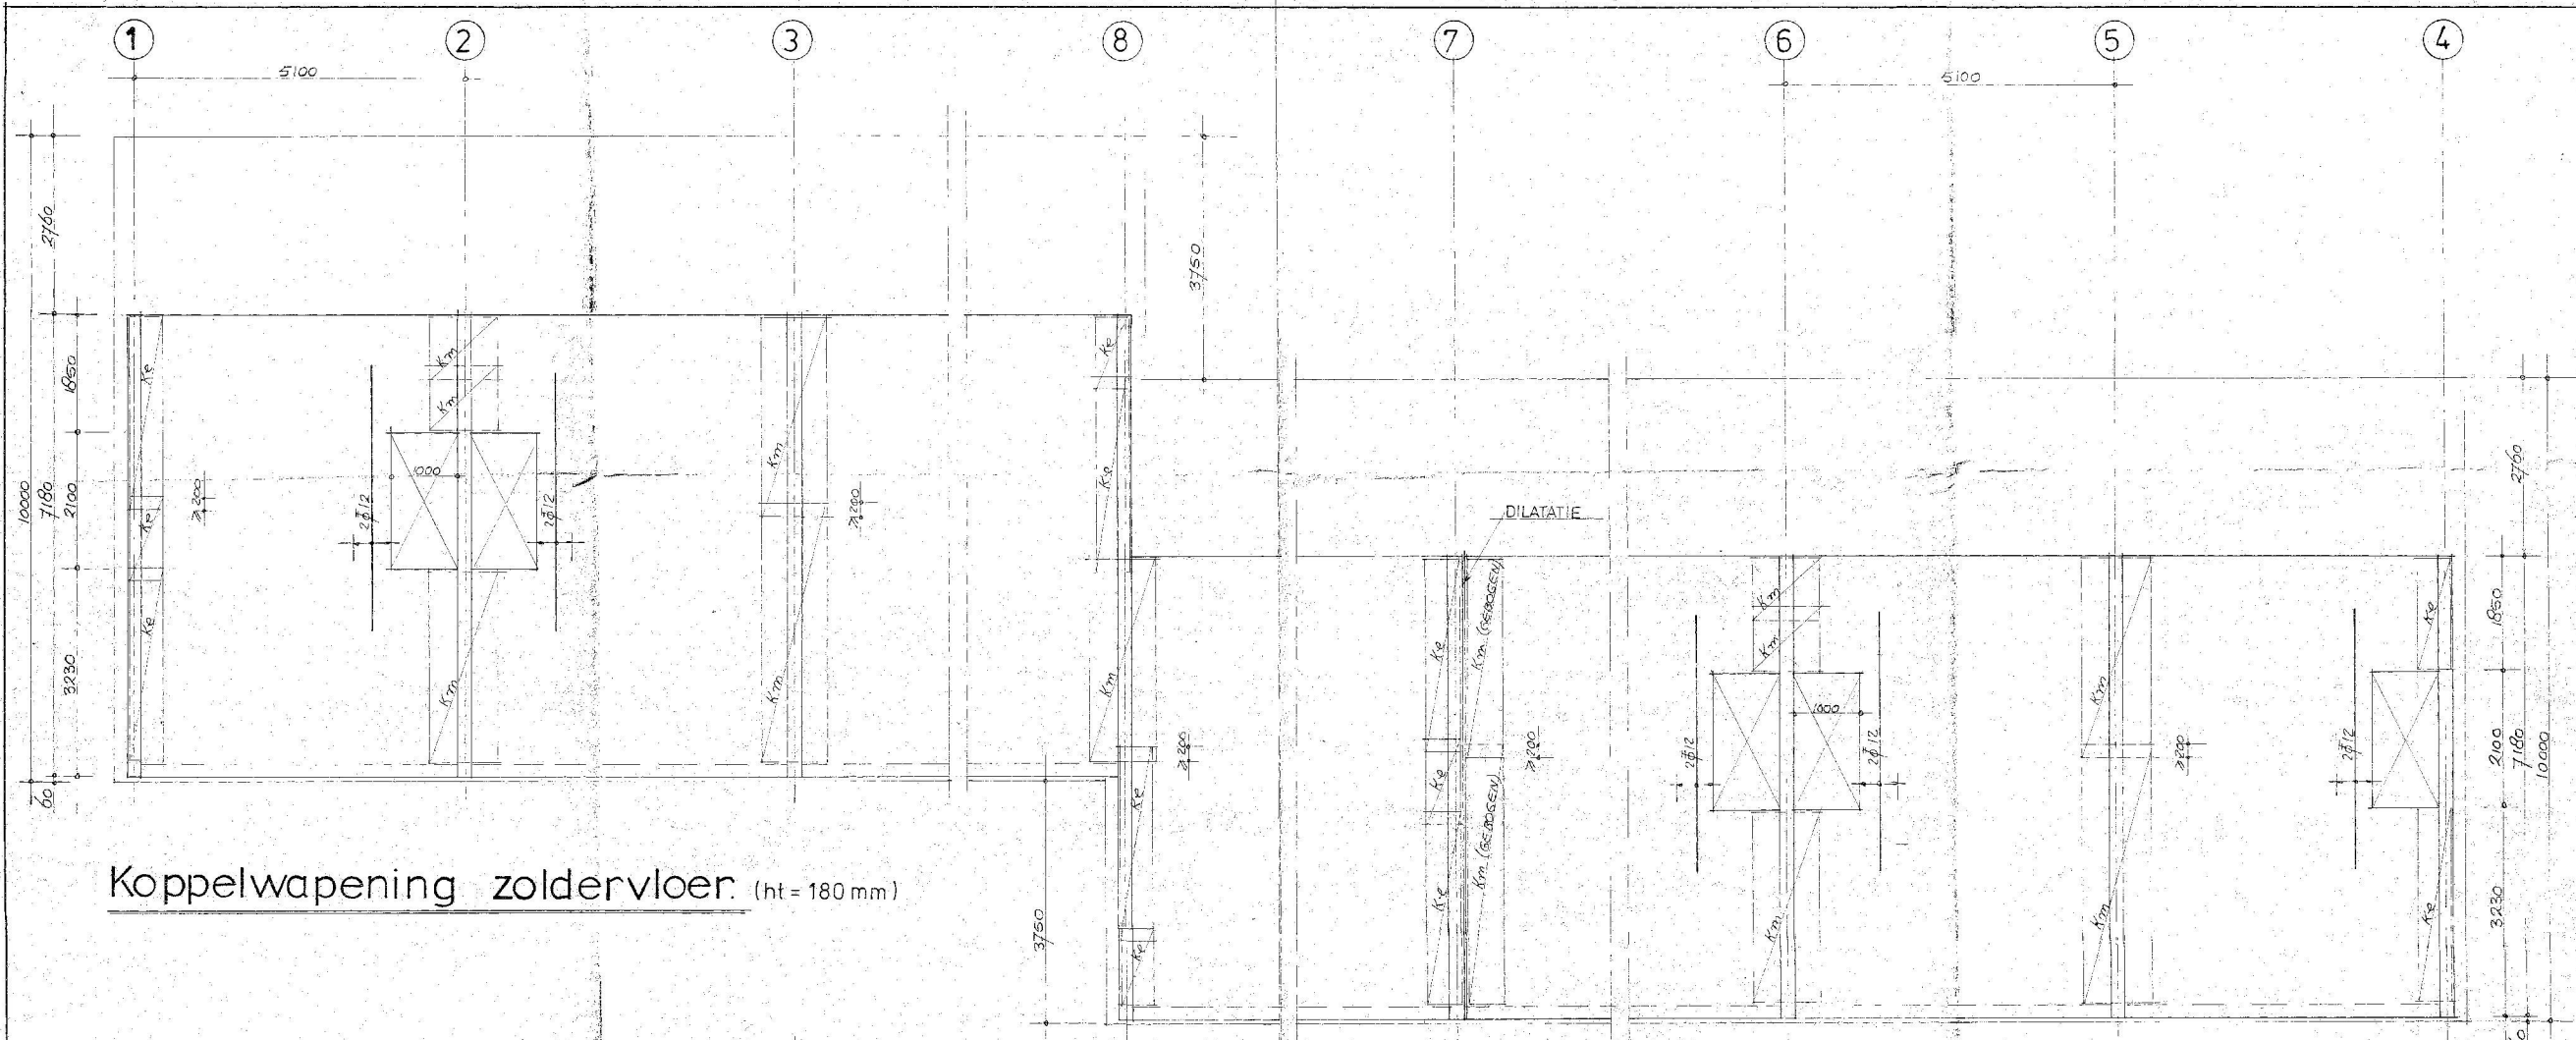

Koppelwapening zoldervloer. (ht=180 mm)

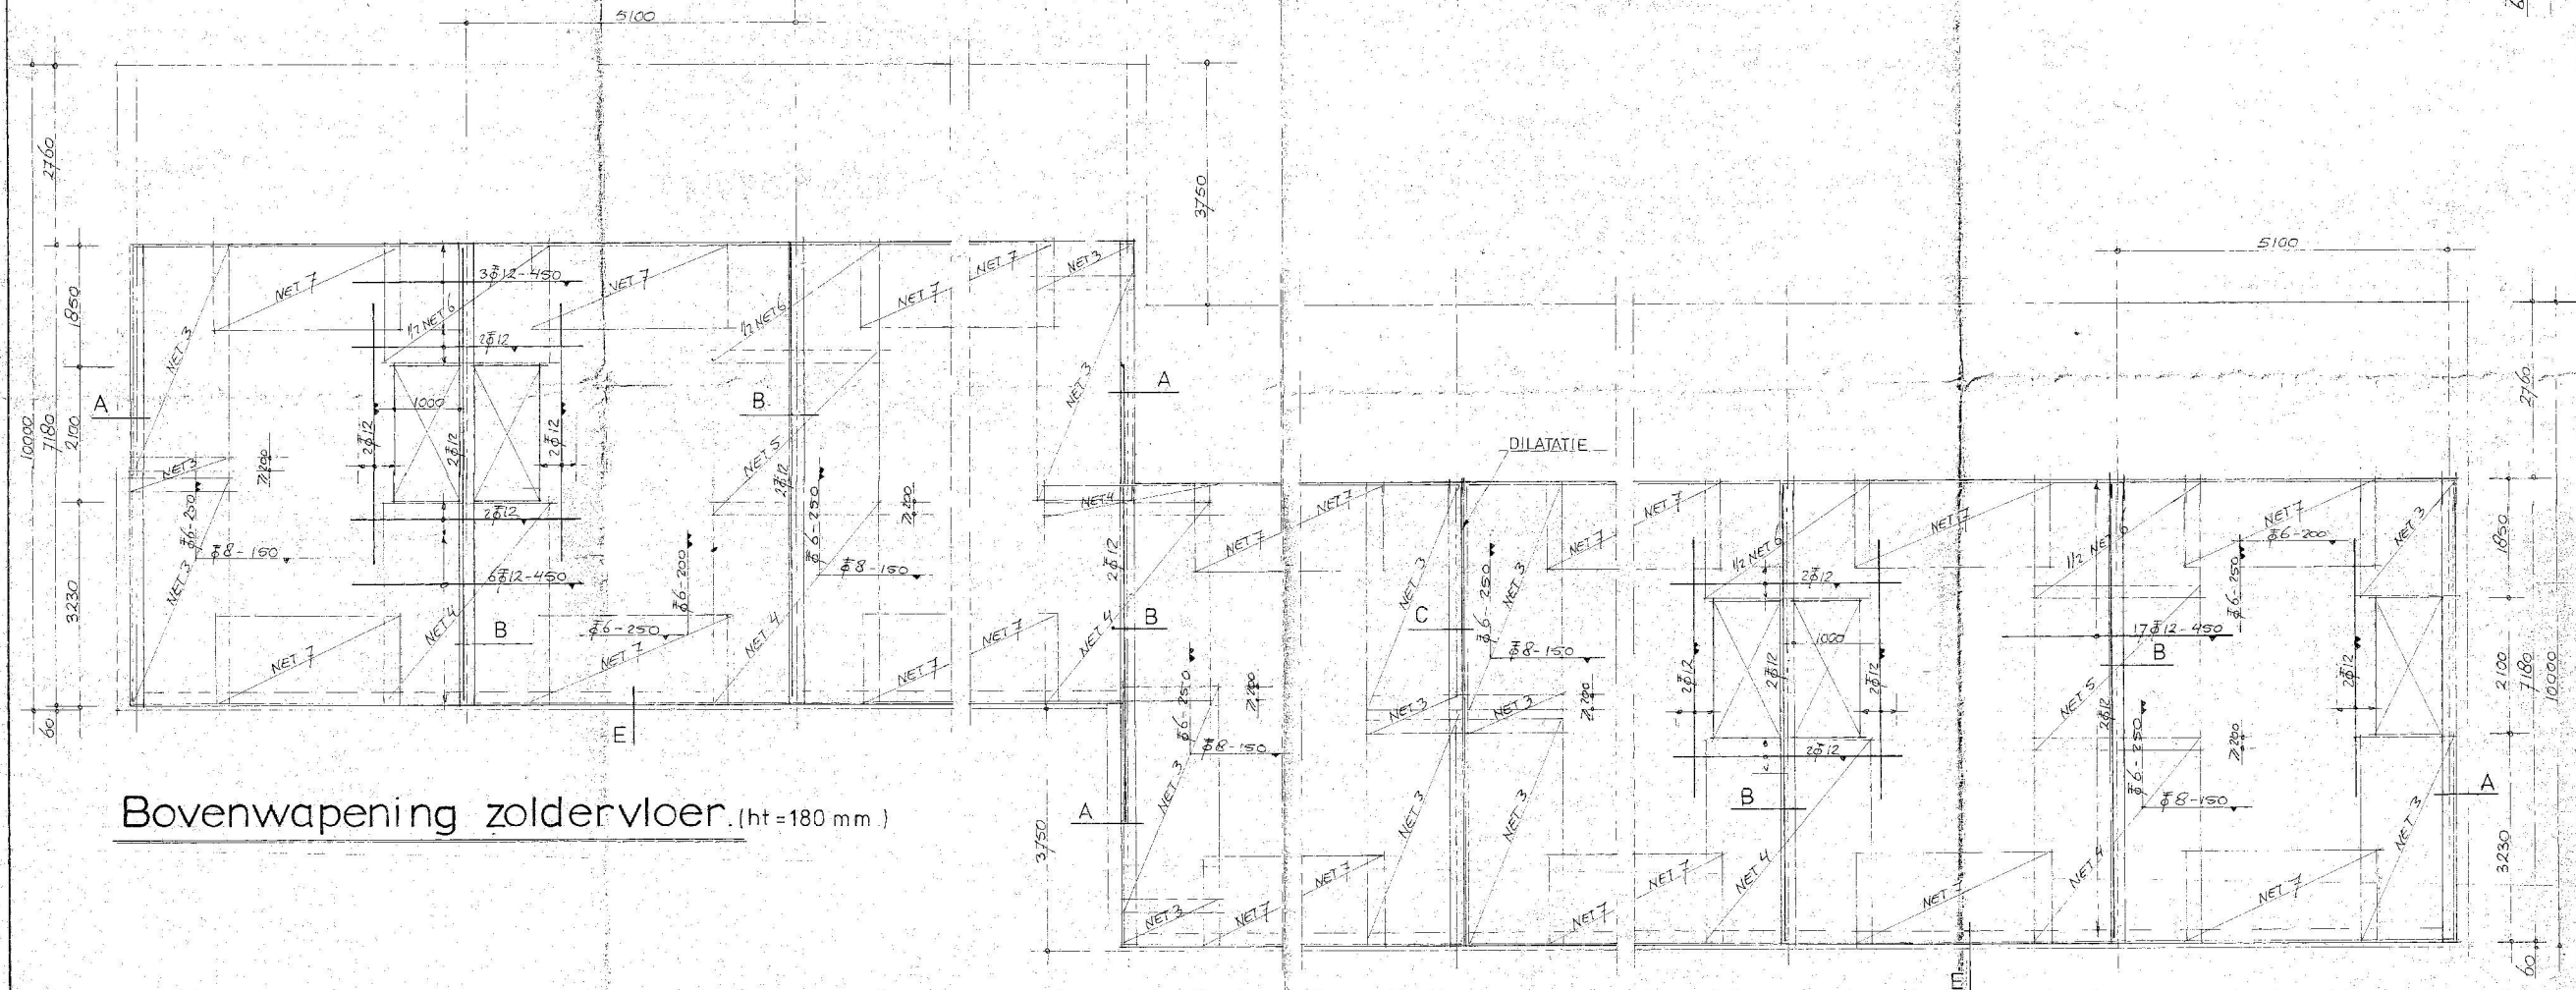

Bovenwapening zoldervloer. (ht=180 mm)

Renvoor:
 Doorgeknipte wapening t.p.v. sparingen
 naast sparingen doorvoeren.
 Overzicht asnummers zie tekening nr. 5.
 Doorsnedens zie tekening nr. 5.

Gezien: 2 JUNI 1988
 Bouw- en Woningtoezicht
 VOORHOUT

Beton:	Kwaliteit B 12.5	Betondekking op betonstaal in mm			
Cement:	Klasse I	Vloeren	Binnen	Auiten	Onzichtbaar
	Portland of hoogoven	Wanden			
	Klasse	Balken			
Staal:	Hoofdwapening FeB 500	Poeren			
	Beugels FeB 500	Kolommen			
	Netten FeB 500				
	Bijleg. wapening FeB 500				
Ontkisten X3 = 20 N/mm²		Sparingen in nader overleg			

Bouw van 19 woningen type M4
 in plan Oosthout B1 te Voorhout

Koppel- en bovenwap. zoldervloer.

Noortlander Bouw b.v.

waak 385-508
 best. 7.
 schaal: 1:50
 getekend: B.v. K.
 datum: 21-4-1988
 conet.: J. den Hartog
 toetsend: 75 x 105
 bewaard: a.
 b. c.
 d. e.
 f. g.

bouwkundig adviesburo h.o. bogaards
 Kerkstraat 2a 2231 CC Rijnburg telefoon 0718-36786